
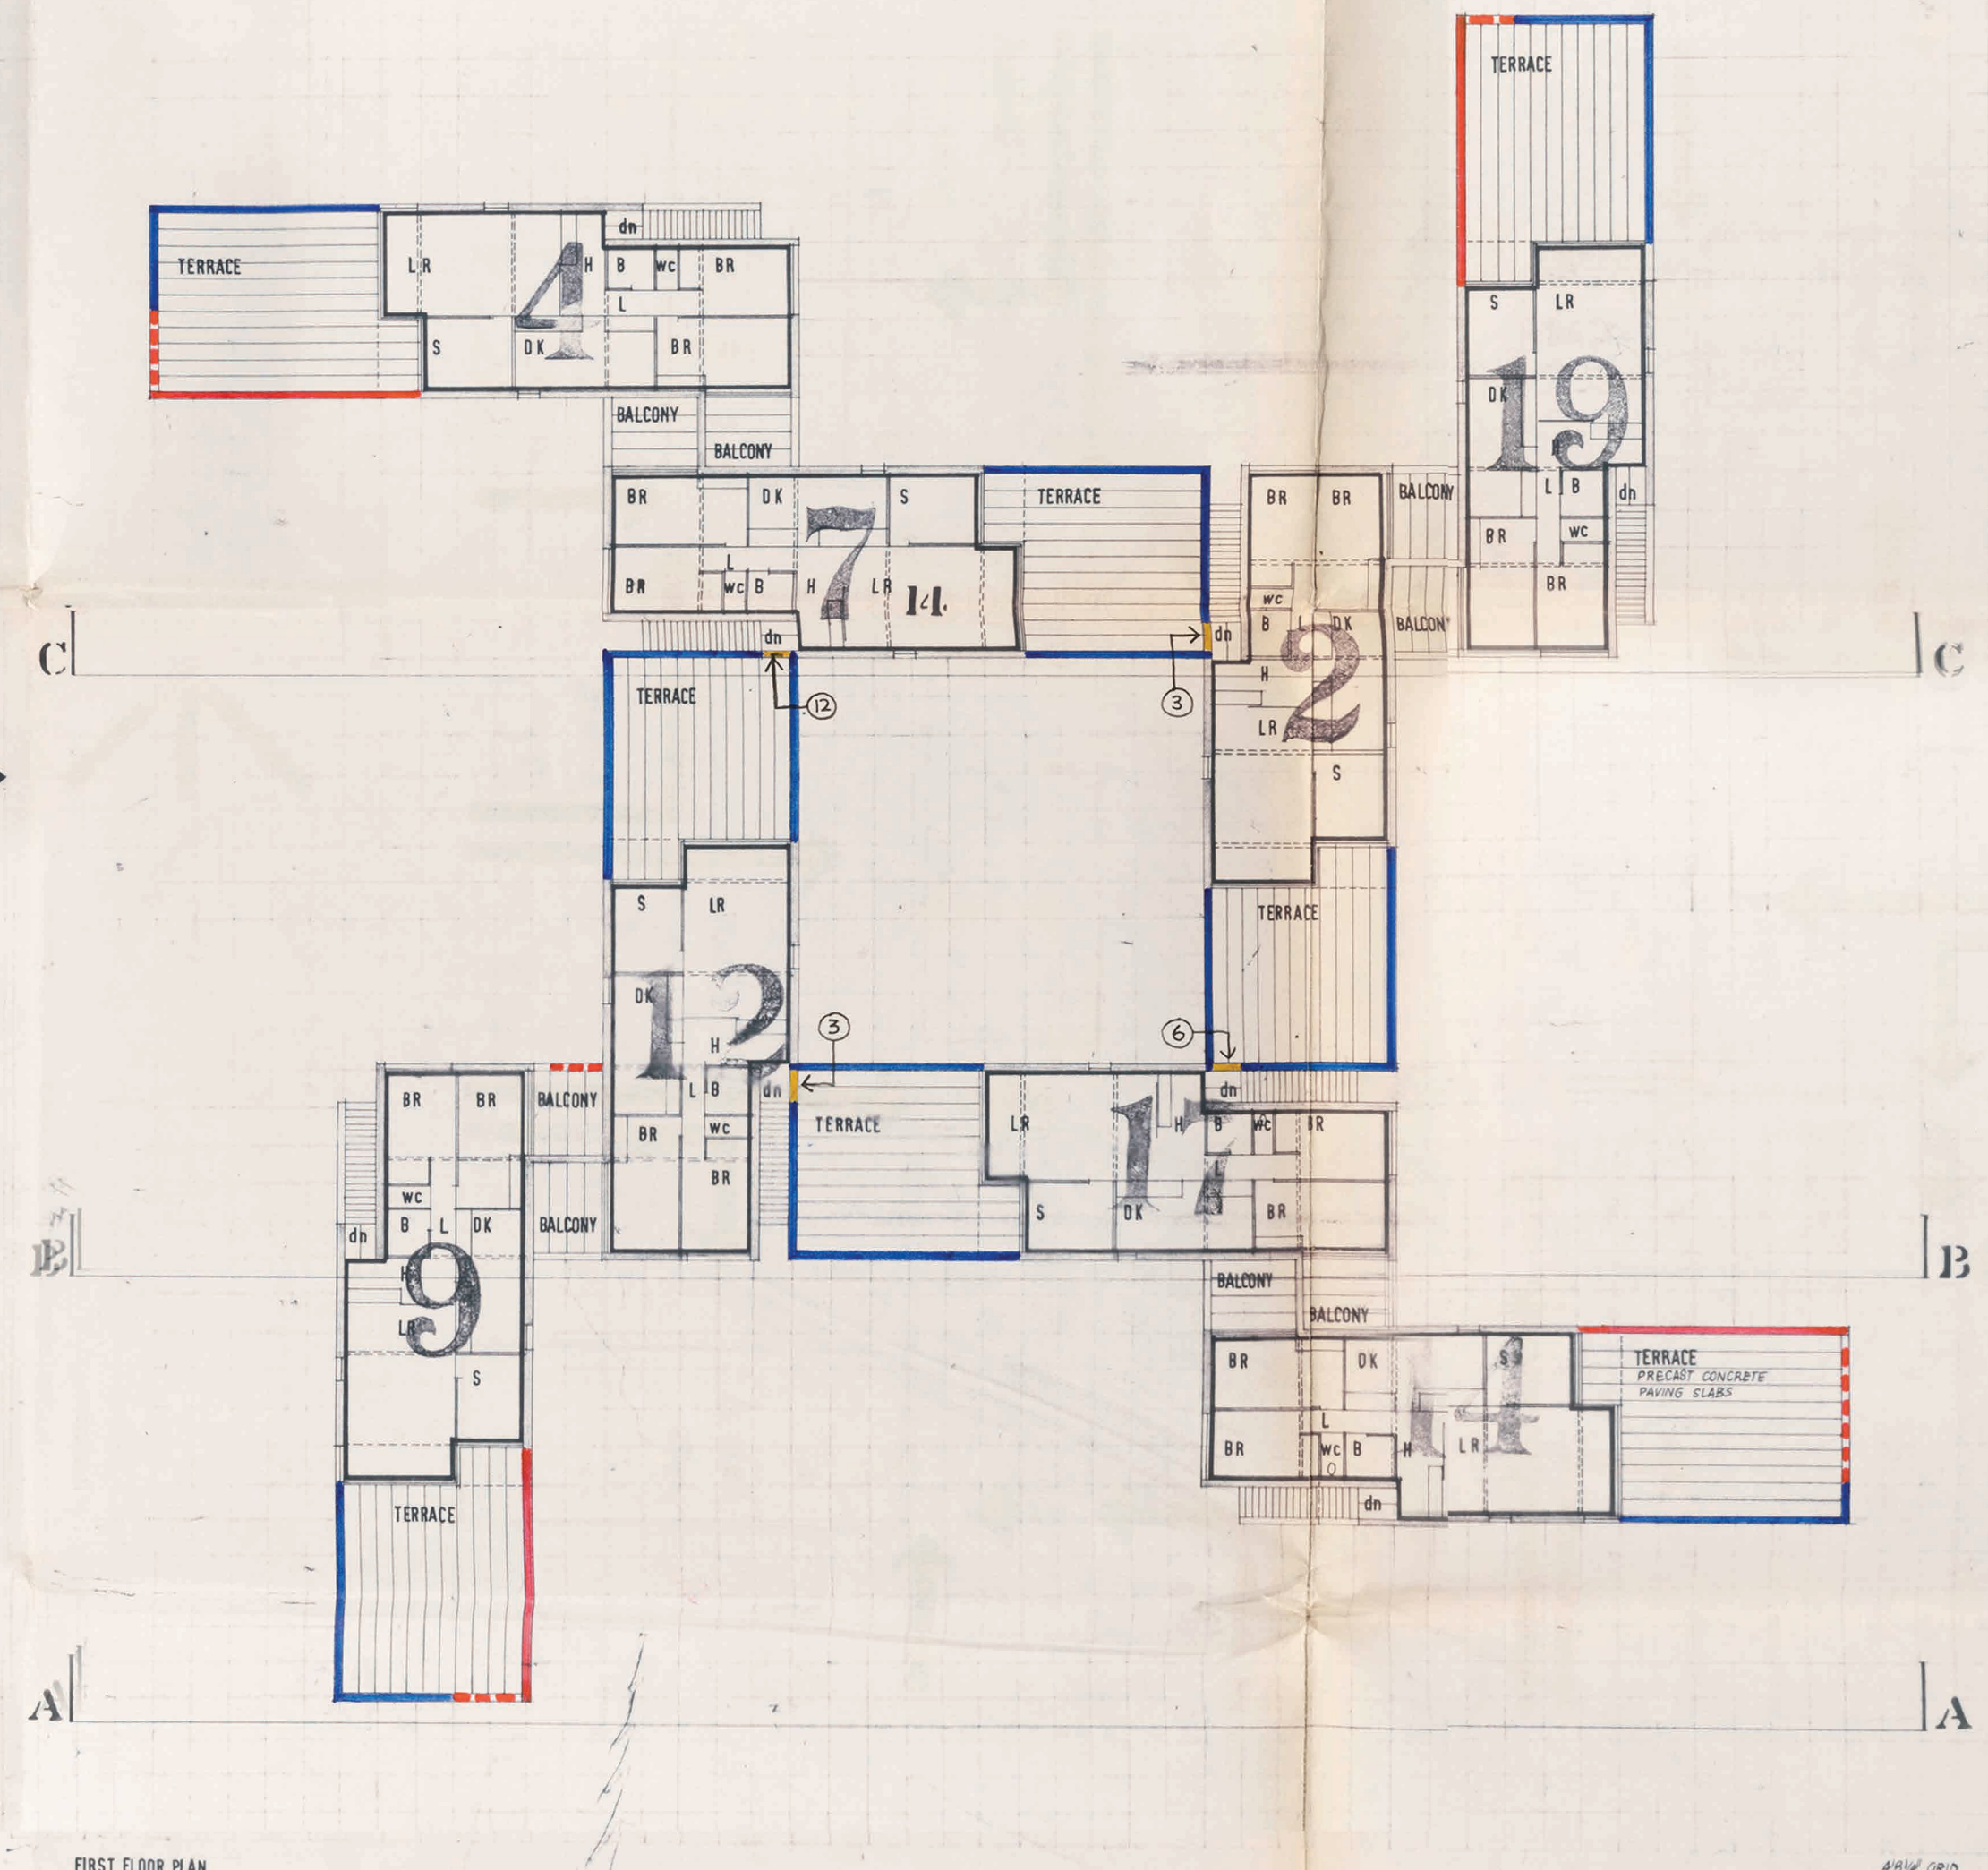
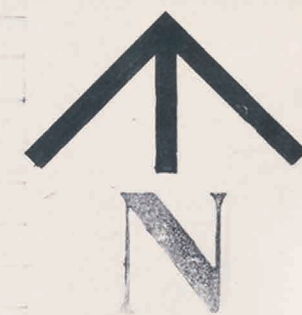


ROAD

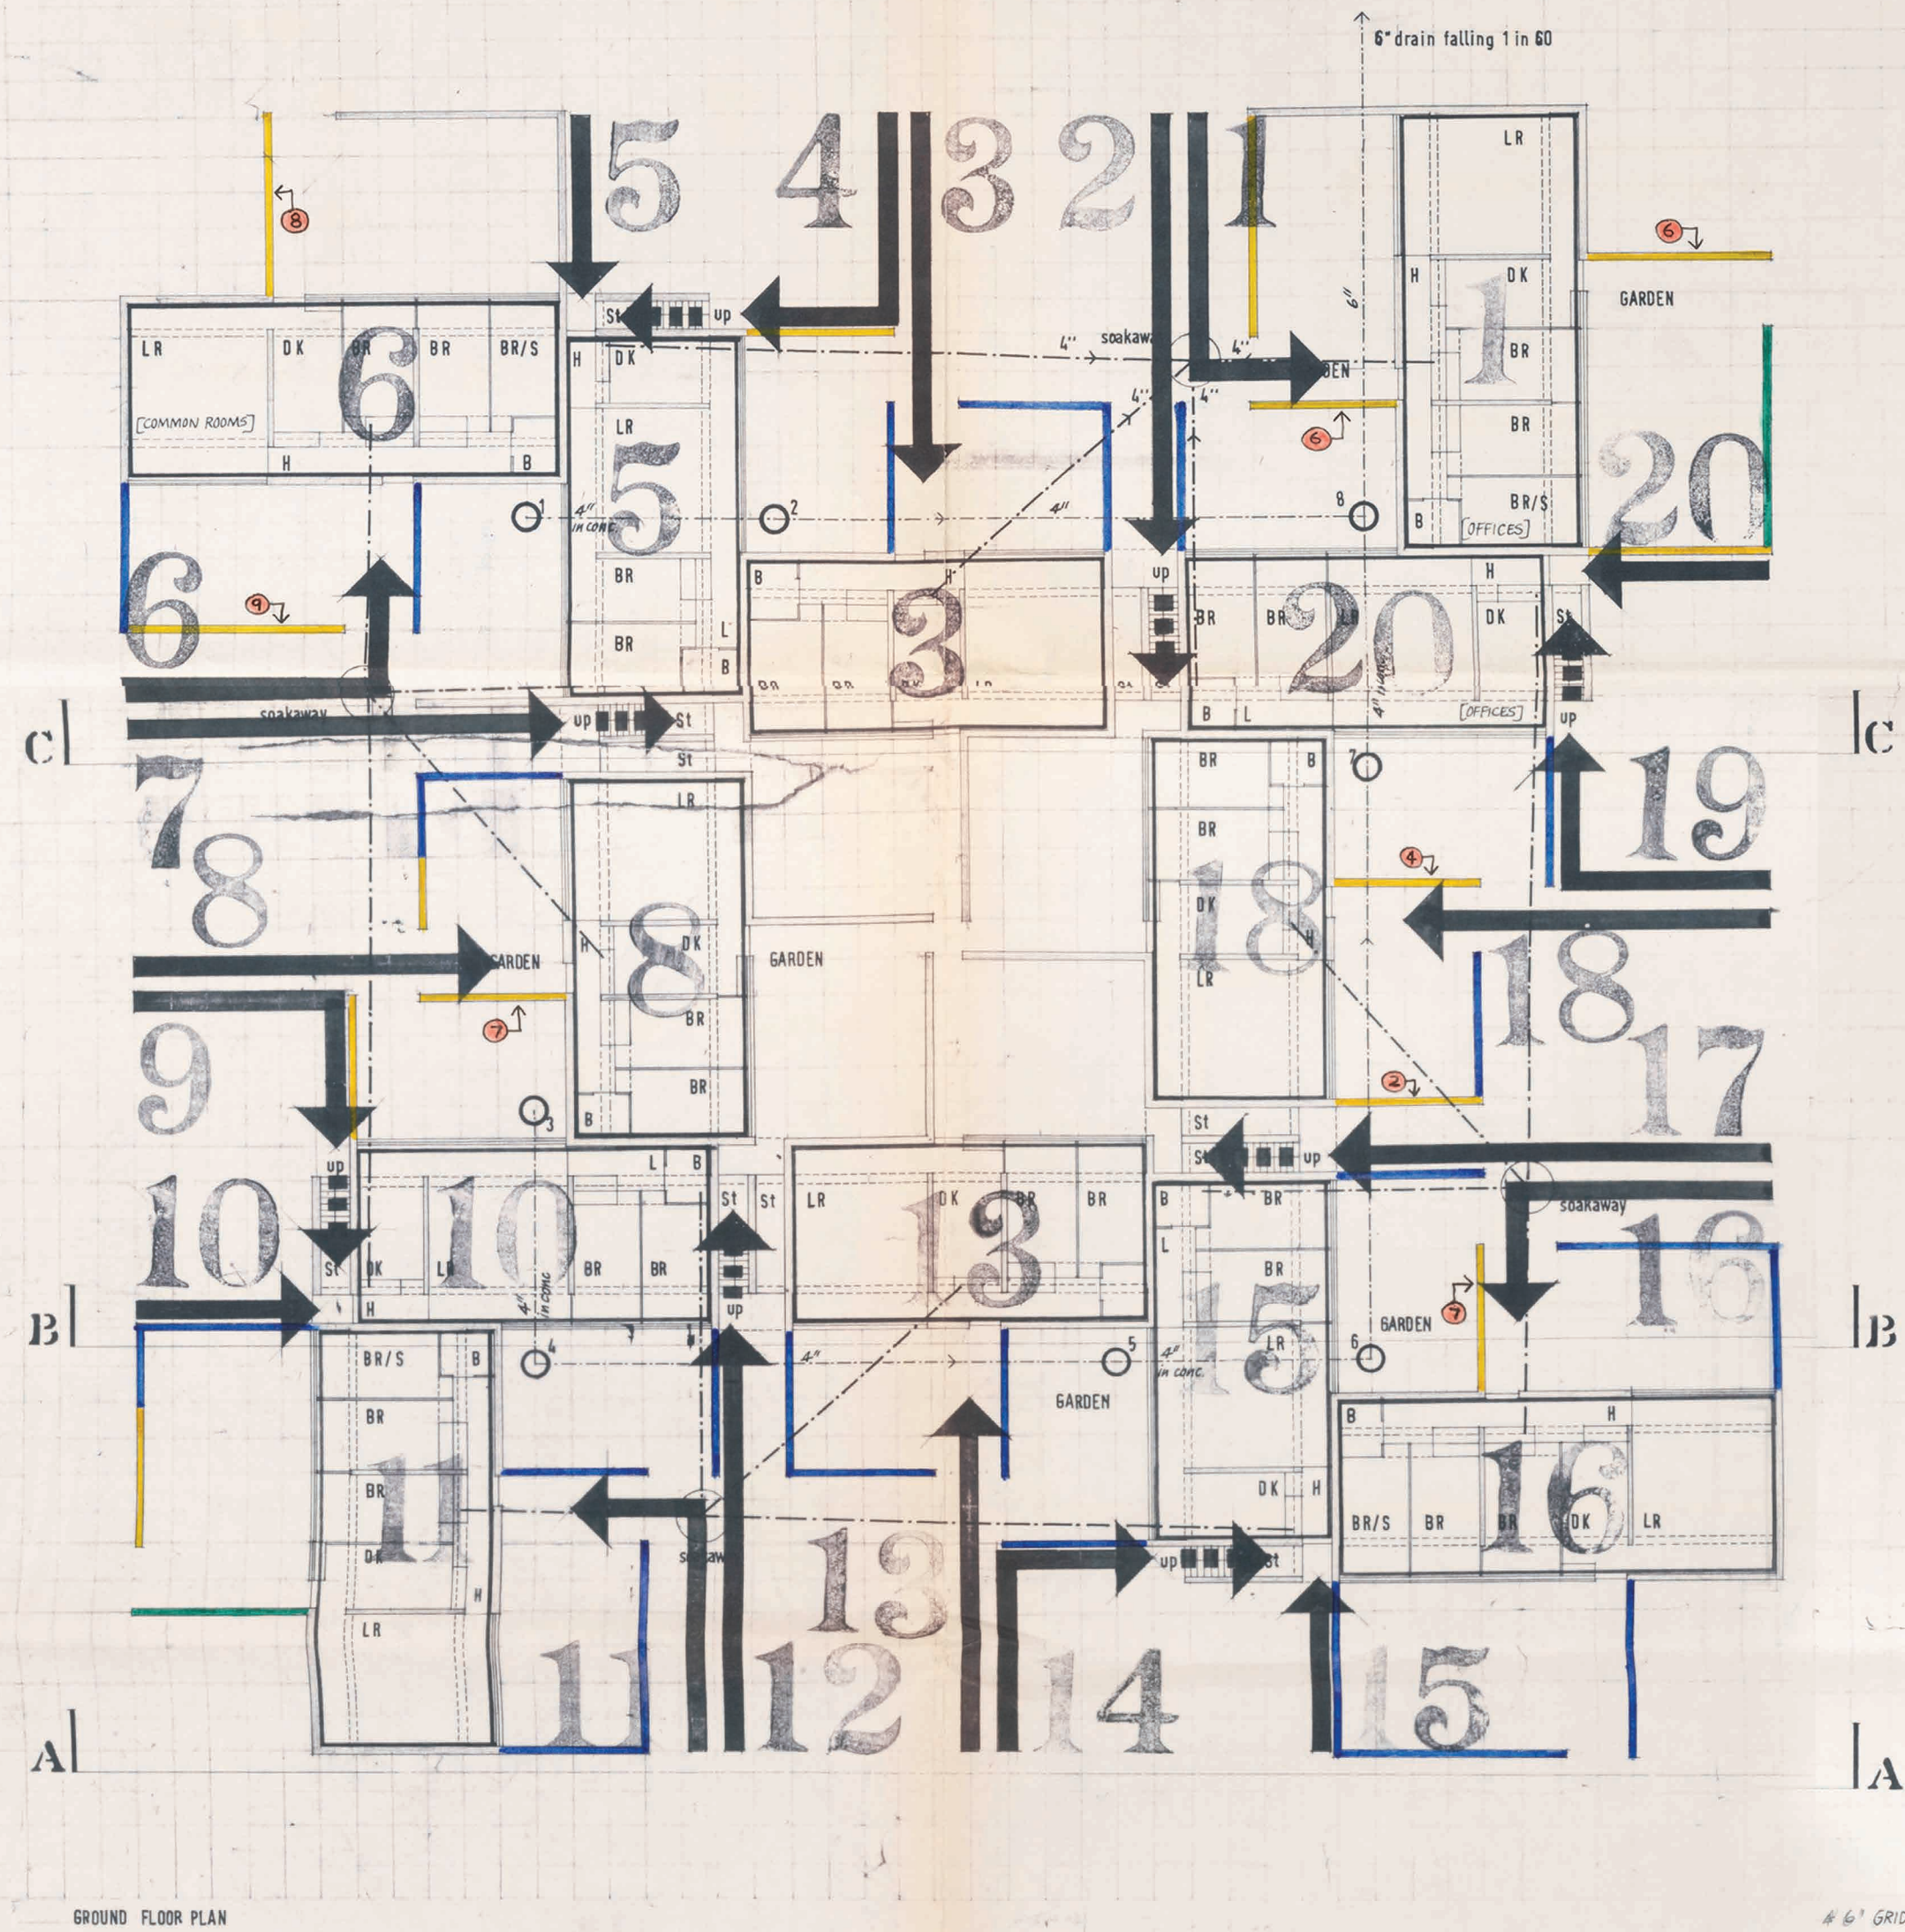

all levels to Ordnance datum

MANHOLE NO	1	2	3	4	5	6	7	8	9	10	11	12	EXISTING SEWER
INVERT LEVEL	67.0	66.0	71.0	70.0	68.0	67.0	65.0	64.0	64.25	60.75	57.75	55.5	54.25
COVER LEVEL	73.0	73.0	73.0	73.0	73.0	73.0	73.0	73.0	71.0	72.0	71.5	71.0	71.0

INT.

- KEY
- LR LIVING ROOM
 - BR BEDROOM
 - DK DINING-KITCHEN
 - S STUDY
 - B BATHROOM
 - H HALL
 - L LOBBY
 - ST STORE

ISSUE	AMENDMENTS	JOB	NO.
A		FLATS	12
B			
C			
D			
E			
F			
G			
		DRAWING PLANS - FLAT NUMBER	
		SCALE 1/16	DATE SEPTEMBER '99
		DRAWN BY PL	CHECKED BY
		RICHARD SHEPPARD, ROBSON & PARTNERS CHARTERED ARCHITECTS, 5, SOUTHAMPTON PLACE, LONDON, W.C.1	